


Деталь обрамления отверстий

(усиление рядового отверстия)

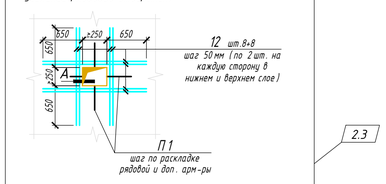

(усиление в зоне опирания края плиты на балку)

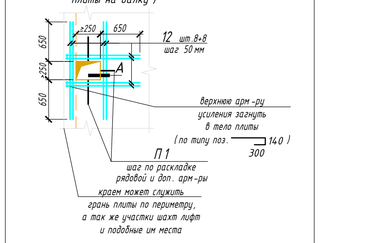

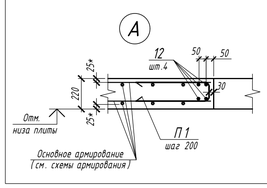

2.3

Ведомость деталей

Поз.	Эскиз
Х1	75, 280, 60
Х2	75, 615, 60
Х3	75, 475, 60
Х4	75, 415, 60
Х5	75, 160, 60
Х6	75, 210, 60
Х7	75, 110, 60
сг1	200, 230, 80, 195, 45°
сг2	200, 200, 220, 100, 120, 45°
сг3	190, 100, 190
сг4	330, 185, 130
сг5	415, 185, 130
сг6	190, 60, 190
П1	500, 135, 500
Ф1	120, 120, 350, 350
Х8	75, 205, 60

2.6

Спецификация к армированию сечений

Поз.	Обозначение	Наименование	Кол.	Масса ед., кг		Приме-чание
		Детали				
		Ф12 А 500 С ГОСТ 34028-2016		2.7		
12		L= м.п.	34.74	0.888		3084.91
		Ф10 А 500 С ГОСТ 34028-2016				
10		L= м.п.	3749	0.617		2313.13
сг1		L= 710	332	0.44		145.44
сг2		L= 960	440	0.59	2.8	260.62
сг3		L= 480	84	0.30		24.88
сг4		L= 650	147	0.40		58.95
сг5		L= 730	104	0.45		46.84
сг6		L= 250	25	0.15	2.9	3.86
П1		L= 1135	716	0.70		501.41
Ф1		L= 1060	823	0.65		538.26
Х8		L= 880	18	0.54		9.77
		Ф8 А 500 С ГОСТ 34028-2016			2.10	
8		L= м.п.	988	0.395		390.26
		Ф6 А 240 ГОСТ 34028-2016				
6		L= м.п.	105	0.222	2.11	23.31
Х1		L= 1030	334	0.23		76.37
Х2		L= 1700	207	0.38		78.12
Х3		L= 1420	19	0.32		5.99
Х4		L= 1300	166	0.29		47.91
Х5		L= 790	46	0.18		8.07
Х6		L= 890	4	0.20		0.79
Х7		L= 690	54	0.15		8.27
1		Уголок 75х75х6 ГОСТ 8509-93 С 255 ГОСТ 27772-2015 м.п.	39	6.89		268.71
КР1	5235-1-1-КЖ 2.1.И-КР1	Каркас плоский КР1	231	1.0		
		Материалы			2.12	
	монолитные сечения (h=220 мм)	БСМ В 25 W4 F75 ГОСТ 7473-2010	93			м³
	зачеканка швов между плитами(5 и 15 мм и сечения по фрагментам на листе 2)	БСМ В 25 W4 F75 ГОСТ 7473-2010	24			м³

Размеры гнутых стержней (типа хомут, скоба, шпилька) указаны в свету по внутренним габаритам. Радиусы гиба арматуры:
А 240 – 1,25d (при d<20), 2d (при d≥20);
А 500 С – 2,5d (при d<20), 4d (при d≥20)


Ведомость расхода стали, кг


Марка элемента	Изделия арматурные								Всего
	Арматура класса								
	А 500С					А 240			
	ГОСТ 34028-2016					ГОСТ 34028-2016			
	Ф12	Ф10	Ф8		Итого	Ф6		Итого	
монолитные сечения	3084.91	3903.17	575.06		7563.1	289.86		289.9	7853.0

2.5

Общие указания по армированию силовой плиты и монолитных участков

1. Работать совместно с л.2 комплекта 5235-1-9-КЖ 2.1
2. Проектную величину защитного слоя для рабочей нижней арматуры обеспечивать пластиковыми фиксаторами, для верхней арматуры - установкой металлических фиксаторов Ф1, Ф2 (в зависимости от высоты сечения монолитных участков) по 2.5 шт/м². Защитный слой для нижней и верхней арматуры 25 мм. Концы стержней рабочей арматуры имеют защитный слой - 20 мм
3. Рабочую арматуру стыковать в нахлест. Величина нахлеста арматуры Ф8 - 400 мм, Ф10 - 500 мм, Ф12 - 600 мм, Ф16 - 800 мм. Расстояние между центрами сечений нахлеста не менее полторы величины нахлеста. В одном сечении допускается стыковать не более 50% всех стыкуемых стержней
4. На чертежах показаны размеры до центров арматурных стержней
5. Размеры, обозначенные знаком "*", показывают величину защитного слоя бетона
6. Позиции сг1...сг6 приварить к полке балки по ГОСТ 14098-2014 Н1-Рш, сварку выполнять согласно требованиям раздела 10 СП 70.13330.2012 "Несущие и ограждающие конструкции"
7. Приварку уголка 75х6 (С255) к основному металлокаркасу выполнять по ГОСТ 5264-80* электродами Э42А по ГОСТ 9466-85 соответственно
8. В стыке между вертикальными колоннами и бетоном монолитных участков, либо бетоном заполнения между сборными плитами, установить прокладку по периметру колонны из сшитого ПЭЭ t=10 мм
9. Перекрытие относится к ответственным конструкциям. К бетонированию монолитных участков приступать после приемки армирования представителем проектной организации, либо представителем строительного контроля технического заказчика
10. Бетонирование конструкций выполнять в соответствии с СП 70.13330.2012 "Несущие и ограждающие конструкции"

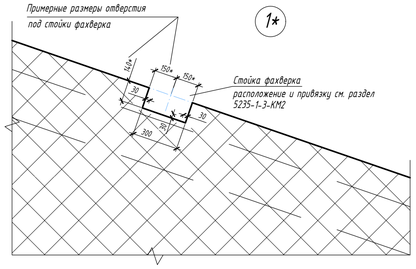

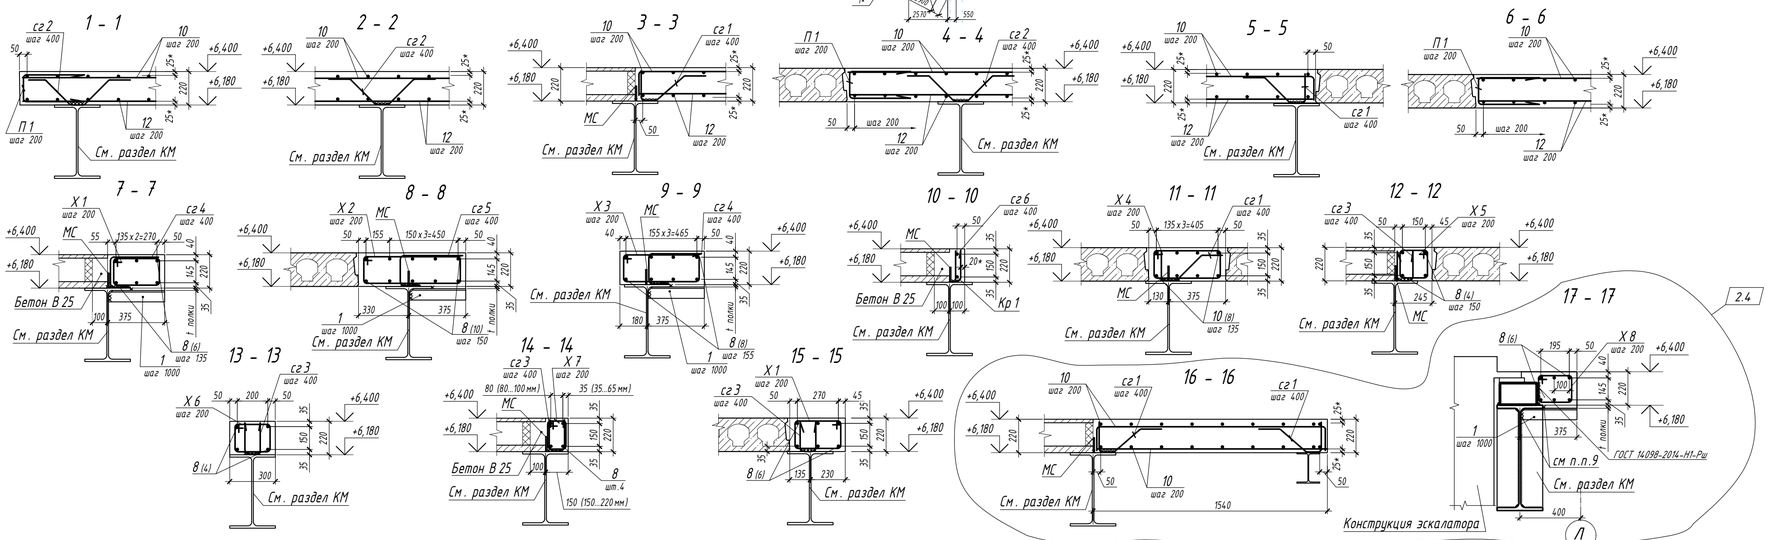

						5235-1-9-КЖ 2.1	
2	12	Изм.	21-25		07.25	Комплекс зданий и сооружений многофункционального ТРЦ с автовокзалом в Чкаловском районе г. Екатеринбурга	
1	-	Нов.	16-24		10.24		
Изм.	Кол. Уч.	Лист	№ док.	Подпись	Дата		
Разработал		Овчукова			03.24	Блок 9	Стадия: Р; Лист: 4; Листов:
Проверил		Коделькова			03.24		
Гл. констр.		Жирных			03.24		
Н. контр.		Жирных			03.24	Схема монолитных участков на отм. +6,400. Сечения 1-1...15-15	УРАЛПРОЕКТДУБРАВА

Согласовано

Взам. инв. N

Подпись и дата

Инв. N подл.

ФОРМАТ А1