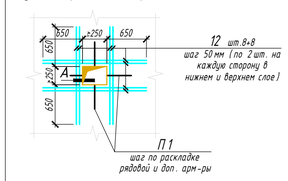
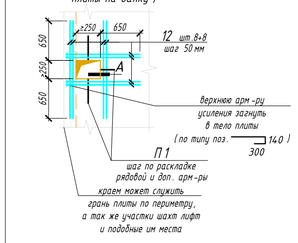
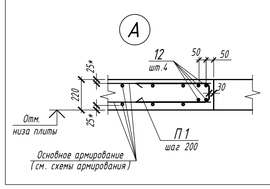
Деталь обрамления отверстий

(усиление рядового отверстия)



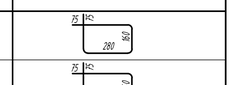
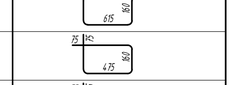
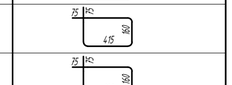
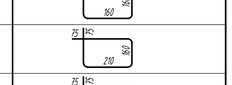
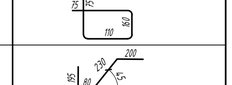
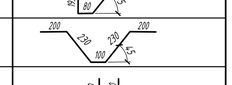
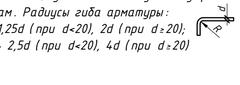
(усиление в зоне опирания края плиты на балку)





2.2

Ведомость деталей

Поз.	Эскиз
Х1	
Х2	
Х3	
Х4	
Х5	
Х6	
Х7	
сг1	
сг2	
сг3	
сг4	
сг5	
сг6	
П1	
Ф1	

Размеры гнутых стержней (типа хомут, скоба, шпилька) указаны в свету по внутренним габаритам. Радиусы гиба арматуры:
А 240 – 1,25d (при d<20), 2d (при d≥20);
А 500 С – 2,5d (при d<20), 4d (при d≥20)



Спецификация к армированию сечений

Поз.	Обозначение	Наименование	Кол.	Масса ед., кг	Приме-чание
		Детали			
		Ф12 А 500 С ГОСТ 34028-2016			2.4
12		L= м.п.	4326	0.888	3841.49
		Ф10 А 500 С ГОСТ 34028-2016			
10		L= м.п.	3948	0.617	2435.92
сг1		L= 710	363	0.44	159.02
сг2		L= 960	452	0.59	267.73
сг3		L= 475	113	0.29	33.12
сг4		L= 650	157	0.40	62.96
сг5		L= 730	104	0.45	46.84
сг6		L= 250	30	0.15	4.63
П1		L= 1135	758	0.70	530.82
Ф1		L= 1060	853	0.65	557.88
		Ф8 А 500 С ГОСТ 34028-2016			
8		L= м.п.	1033	0.395	408.04
		Ф6 А 240 ГОСТ 34028-2016			
6		L= м.п.	101	0.222	22.42
Х1		L= 1030	266	0.23	60.82
Х2		L= 1700	207	0.38	78.12
Х3		L= 1420	45	0.32	14.19
Х4		L= 1300	166	0.29	47.91
Х5		L= 790	53	0.18	9.30
Х6		L= 890	39	0.20	7.71
Х7		L= 690	95	0.15	14.55
1		Уголок 75х75х6 ГОСТ 8509-93 / С255 ГОСТ 27772-2015 м.п.	39	6.89	268.71
КР1	5235-1-1-КЖ2.1.И-КР1	Каркас плоский КР1	225	1.0	
		Материалы			2.5
	монолитные сечения (h=220 мм)	БСМ В25 W4 F75 ГОСТ 7473-2010	94		м³
	зачеканка швов между плитами (5 и 15мм и сечения по фрагментам на листе 2)	БСМ В25 W4 F75 ГОСТ 7473-2010	24		м³


Ведомость расхода стали, кг


Марка элемента	Изделия арматурные								Всего
	Арматура класса								
	А 500С					А 240			
	ГОСТ 34028-2016					ГОСТ 34028-2016			
	Ф12	Ф10	Ф8		Итого	Ф6		Итого	
монолитные сечения	3841.5	4098.9	588.0		8528.4	295.0		295.0	8823.4

2.3

Общие указания по армированию силовой плиты и монолитных участков

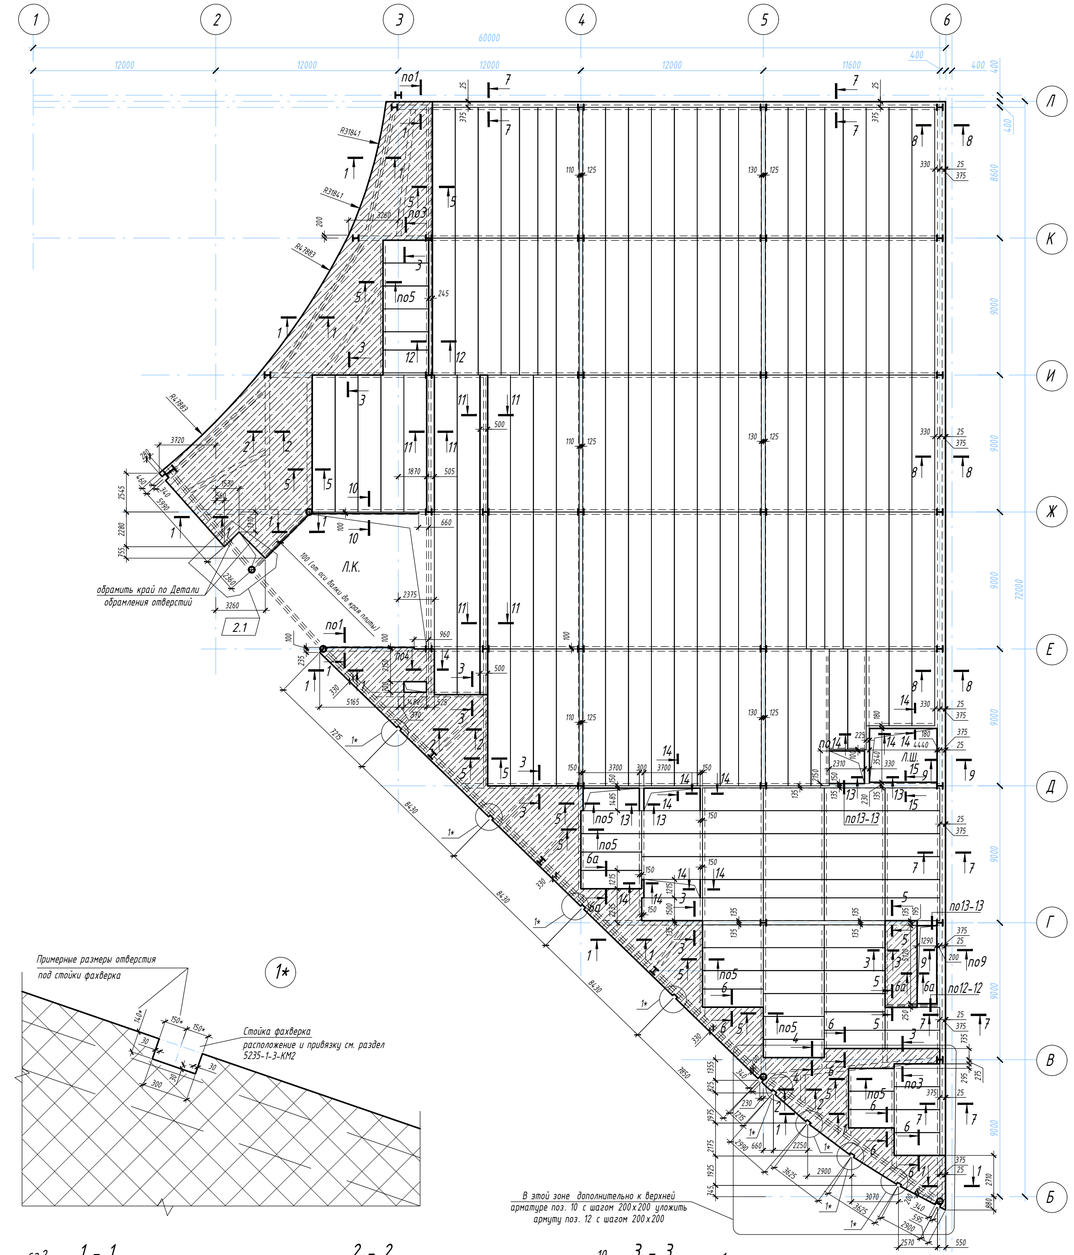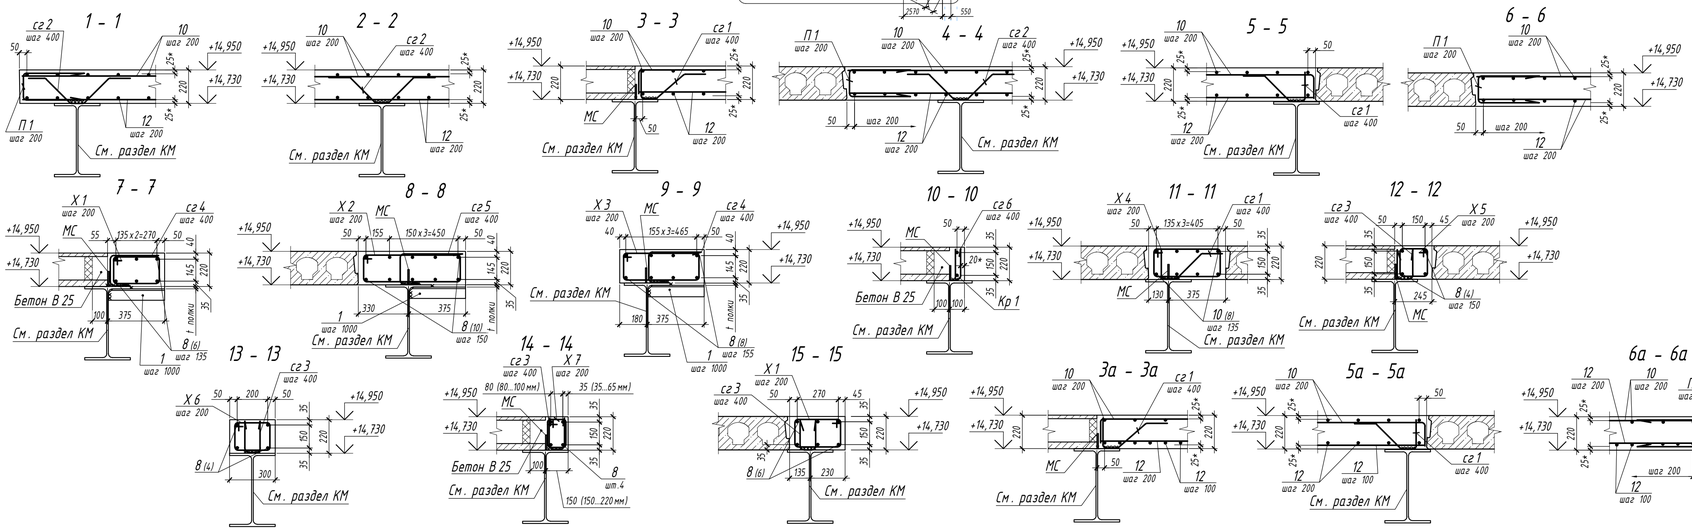1. Работать совместно с л.2 комплекта 5235-1-9-КЖ2.2
2. Проектную величину защитного слоя для рабочей нижней арматуры обеспечивать пластиковыми фиксаторами, для верхней арматуры - установкой металлических фиксаторов Ф1, Ф2 (в зависимости от высоты сечения монолитных участков) по 2.5шт/м². Защитный слой для нижней и верхней арматуры 25 мм. Концы стержней рабочей арматуры имеют защитный слой - 20 мм
3. Рабочую арматуру стыковать в нахлест. Величина нахлеста арматуры Ф8 - 400мм, Ф10 - 500мм, Ф12 - 600мм, Ф16 - 800 мм. Расстояние между центрами сечений нахлеста не менее полторы величины нахлеста. В одном сечении допускается стыковать не более 50% всех стыкуемых стержней
4. На чертежах показаны размеры до центров арматурных стержней
5. Размеры, обозначенные знаком "*", показывают величину защитного слоя бетона
6. Позиции сг1...сг6 приварить к полке балки по ГОСТ 14098-2014 Н1-Рш, сварку выполнять согласно требованиям раздела 10 СП 70.13330.2012 "Несущие и ограждающие конструкции"
7. Приварку уголка 75х6 (С255) к основному металлокаркасу выполнять по ГОСТ 5264-80* электродами Э42А по ГОСТ 9466-85 соответственно
8. В стыке между вертикальными колоннами и бетоном монолитных участков, либо бетоном заполнения между сборными плитами, установить прокладку по периметру колонны из сшитого ПЭП t=10мм
9. Перекрытие относится к ответственным конструкциям. К бетонированию монолитных участков приступать после приемки армирования представителем проектной организации, либо представителем строительного контроля технического заказчика
10. Бетонирование конструкций выполнять в соответствии с СП 70.13330.2012 "Несущие и ограждающие конструкции"





Согласовано
Взам. инв. N
Подпись и дата
Инв. N подл.

						5235-1-9-КЖ2.2
2	5	Изм.	21-25		07.25	Комплекс зданий и сооружений многофункционального ТРЦ с автовокзалом в Чкаловском районе г. Екатеринбурга
1	-	Нов.	16-24		11.04.24	
Изм.	Кол.Уч.	Лист	№ док.	Подпись	Дата	
Разработал		Овчукова			03.24	Блок 9 — Стадия: Р; Лист: 4; Листов:
Проверил		Кобелькова			03.24	
Гл. констр.		Жирных			03.24	
Н. контр.		Жирных			03.24	Схема монолитных участков на отм. +14,950. Сечения 1-1...15-15 — УРАЛПРОЕКТДУБРАВА

ФОРМАТ А1